Жауапкершілігі шектеулі серіктестігі «ADAL Stroy Limited»

Товарищество с ограниченной ответственностью «ADAL Stroy Limited»

Алматы қаласы, Алатау аумағы, Улжан 1 ықшам ауданы, Ақжазық көшесі № 11

МҚЛ №22002089
ГСЛ №22002089

г. Алматы, Алатауский район, мкр. Улжан 1, ул. Акжазык 11

Эскизный проект

детского сада и столовой

Алматинская обл., Енбекшиказахский район,
Каракемерский с/о., с.Талдыбулак, ул.Жамангараев, №77А

Заказчик: Толендиева Мейрамгуль Билибайевна

Директор ТОО "ADAL Stroy Limited" _____ */Алмабек А.О.*

г.Алматы 2024г.

Сканировано с CamScanner

Ведомость основного комплекта чертежей марки АР

Лист	Наименование	Примечание
1	Ведомость чертежей	
1.1	Общие данные	
1.2	Схема генерального плана М1:500	
1.3	Схема инженерных сетей М1:500	
2	План на отм. 0.000	
3	План на отм. 3.000	
4-5	Фасады	
6	Разрез 1-1	
7	План кровли	
8	План на отм. 0.000	
9	Фасады	
10	Разрез 1-1	
11	План кровли	

Изм.	Кол.уч	Лист	№док.	Подп.	Дата	06-2024-ЭП		
						Алматинская обл. Енбекшиказахский р-н. Каракемерский с/о., с.Талдыбулак, ул.Жамангараев, №77А		
						Заказчик: Толендиева М.Б.	Стадия	Лист	Листов
Разработал		Калибеков Б.					ЭП	1	11
						Ведомость чертежей	ТОО "ADAL Stroy Limited" Гос.Лиц МКЛ №22002089		

Сканировано с CamScanner

Общие указания

1. Эскизный проект "детского сада и столовой" разработан на основании задания на проектирование и действующих норм и правил.

2. Месторасположение участка:
Детский сад, столовая, расположены по адресу: Алматинская область, Енбекшиказахский район, Каракемерский с/о., с.Талдыбулак, ул.Жамангараев, №77А

3. Природно-климатические условия площадки строительства:
- район строительства
Каракемерский с/о.
- строительно климатический район
IIIВ (СНиП РК 2.04.01-2010)
- температура воздуха наиболее холодной пятидневки
-21 С°(СНиП РК 2.04.01-2010)
- нормативное ветровое давление на уровне 10 м над поверхностью земли для III ветрового района
0,38 кПа (СНиП 2.01-07-85)
- нормативный вес снегового покрова на 1м2 горизонтальной для II снегового района
0,7 кПа (СНиП 2.01-07-85)
- согласно СН РК 2.03-30-2006 категория грунтов по сейсмическим свойствам I
- максимальная глубина промерзания на площадке
0,95 м
- сейсмичность района строительства
9 баллов
(согласно СН РК 2.03-07-2001)

4. Степень огнестойкости здания II (СНиП 2.02-05-2009)

5. Уровень ответственности здания (сооружения) II (нормальный)

6. Класс функциональной пожарной опасности здания Ф1.4

7. Класс конструктивной пожарной опасности здания С1

8. Конструктивное решение здания:
- фундамент ленточный железобетонный;
- стены наружные - сплитерные блоки;
- внутренние перегородки - сплитерные блоки, гипсокартон;

9. Гидроизоляцию бетонных поверхностей выполнить жидкой битумной мастикой за 2 раза.

10. Наружная отделка фасада:
- стены - штукатурка "Мюнхенка";
- кровля - металлопрофиль;
- окна - металлопластиковые, цвет - белый;
- двери наружные - металлические утепленные, внутренние - деревянные.

11. Вокруг здания предусмотреть бетонную отмостку по щебеночному основанию шириной 1000 мм.

Архитектурные решения

Детский сад представляет собой двухэтажное здание.
Здание квадратное в плане с размерами в осях 17,70м х 17,70 м.
Высота 1-го этажа (от пола до потолка) - 2.80м
Высота 2-го этажа (от пола до потолка) - 2.80м
Фундаменты - железобетон толщиной 400 мм.
Внутренние несущие стены и перегородки - сплитерные блоки, гипсокартон;
Перекрытие - армированное монолитное.
Крыша - односкатная.
Кровля - металлопрофиль по деревянным стропилам.
Окна приняты из профилей ПВХ, белого цвета. Остекление двойное.
Входная дверь - металлическая утепленная по типу ГОСТ 31173-2003 с приспособлениями для самозакрывания и уплотнением в притворах.
Внутренние двери деревянные по типу ГОСТ 6629-88.
Наружная отделка фасадов - штукатурка "Мюнхенка".
Цокольная часть здания декоративный облицовочный кирпич.
Вокруг здания предусмотрена бетонная отмостка шириной 1000 мм.

Столовая представляет собой одноэтажное здание.
Здание прямоугольное в плане с размерами в осях 4,80м х 11,60 м.
Высота 1-го этажа (от пола до потолка) - 2.70м
Фундаменты - железобетон толщиной 300 мм.
Внутренние несущие стены и перегородки - сплитерные блоки;
Перекрытие - деревянное.
Крыша - односкатная.
Кровля - металлопрофиль по деревянным стропилам.
Окна приняты из профилей ПВХ, белого цвета. Остекление двойное.
Входная дверь - металлическая утепленная по типу ГОСТ 31173-2003 с приспособлениями для самозакрывания и уплотнением в притворах.
Внутренние двери деревянные по типу ГОСТ 6629-88.
Наружная отделка фасадов - штукатурка "Мюнхенка".
Цокольная часть здания декоративный облицовочный кирпич.
Вокруг здания предусмотрена бетонная отмостка шириной 1000 мм.

						06-2024-ЭП			
Изм.	Кол.уч.	Лист	№док.	Подп.	Дата	Алматинская обл. Енбекшиказахский р-н. Каракемерский с/о., с.Талдыбулак, ул.Жамангараев, №77А			
						Заказчик: Толендиева М.Б.	Стадия	Лист	Листов
							ЭП	1.1	11
Разработал		Калибеков Б.				Общие указания	ТОО "ADAL Stroy Limited" Гос.Лиц МКЛ №22002089		

Сканировано с CamScanner

Схема генерального плана
М1:500

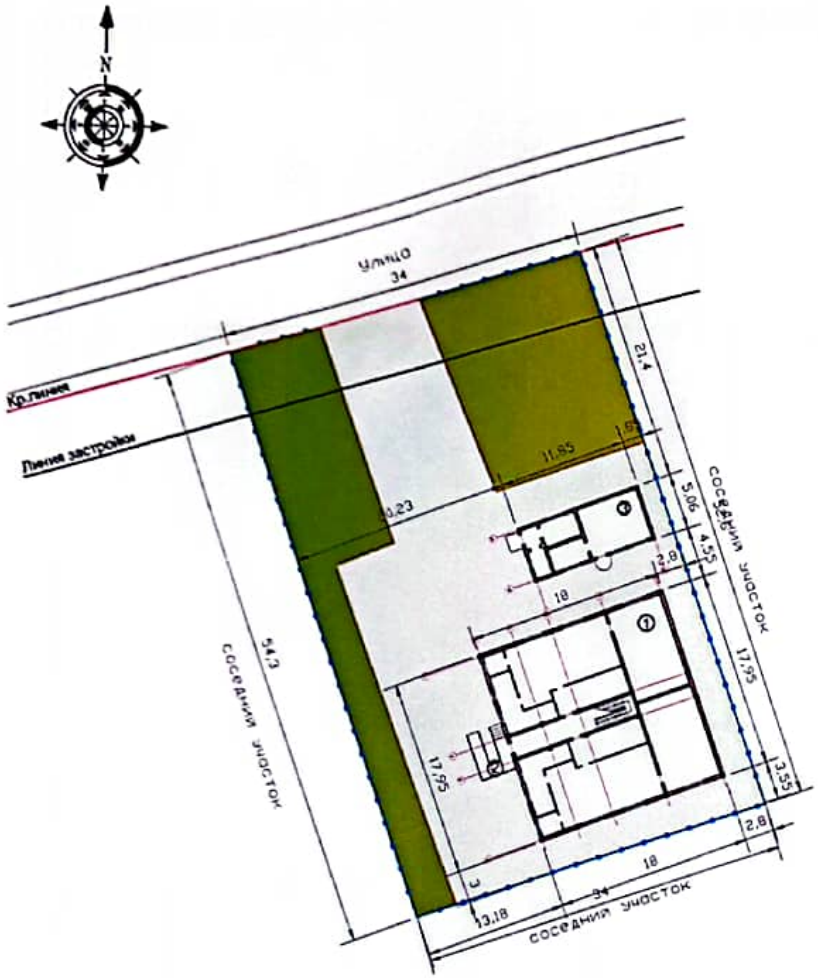

Ситуационный план
М1:2000

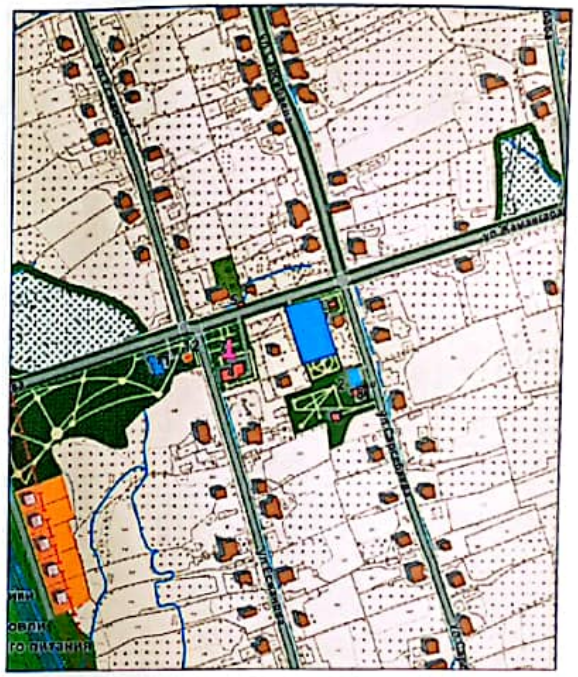

ТЕХНИКО ЭКОНОМИЧЕСКИЕ ПОКАЗАТЕЛИ

№ п.п.	Наименование	Площадь застройки м2
1	Площадь земельного участка	1798,0
2	Площадь застройки	396,5
3	Площадь покрытий (асфальт)	300,0
4	Площадь озеленения	1101,5

Экспликация зданий и сооружений

№ п.п.	Наименование	Кол-во	Площадь застройки м2	Примечание
1	Здание детского сада	1	324,9	Проектируемый
2	Крыльцо	1	11,7	Проектируемый
3	Кухня	1	59,9	Проектируемый

Условные обозначения:

- *Улицы и проезды*
- *Озеленение*
- *Асфальтовое покрытие*
- *Бордюры*
- *Деревья*

Изм.	Кол.уч.	Лист	№док.	Подпись	Дата
Разраб.		Калибеков Е.			

06-2024-ЭП

Алматинская обл. Енбекшиказахский р-н.
Каракенерский с/о., с.Талдыбулак, ул.Жанангараев, №77А

Заказчик: Толендиева М.Б.

Стадия	Лист	Листов
ЭП	1.2	11

Схема генерального плана
М1:500

ТОО "ADAL Stroy Limited"
Гос.Лиц МКЛ №22002089

Сканировано с CamScanner

План на отм. 0.000
М 1:1000

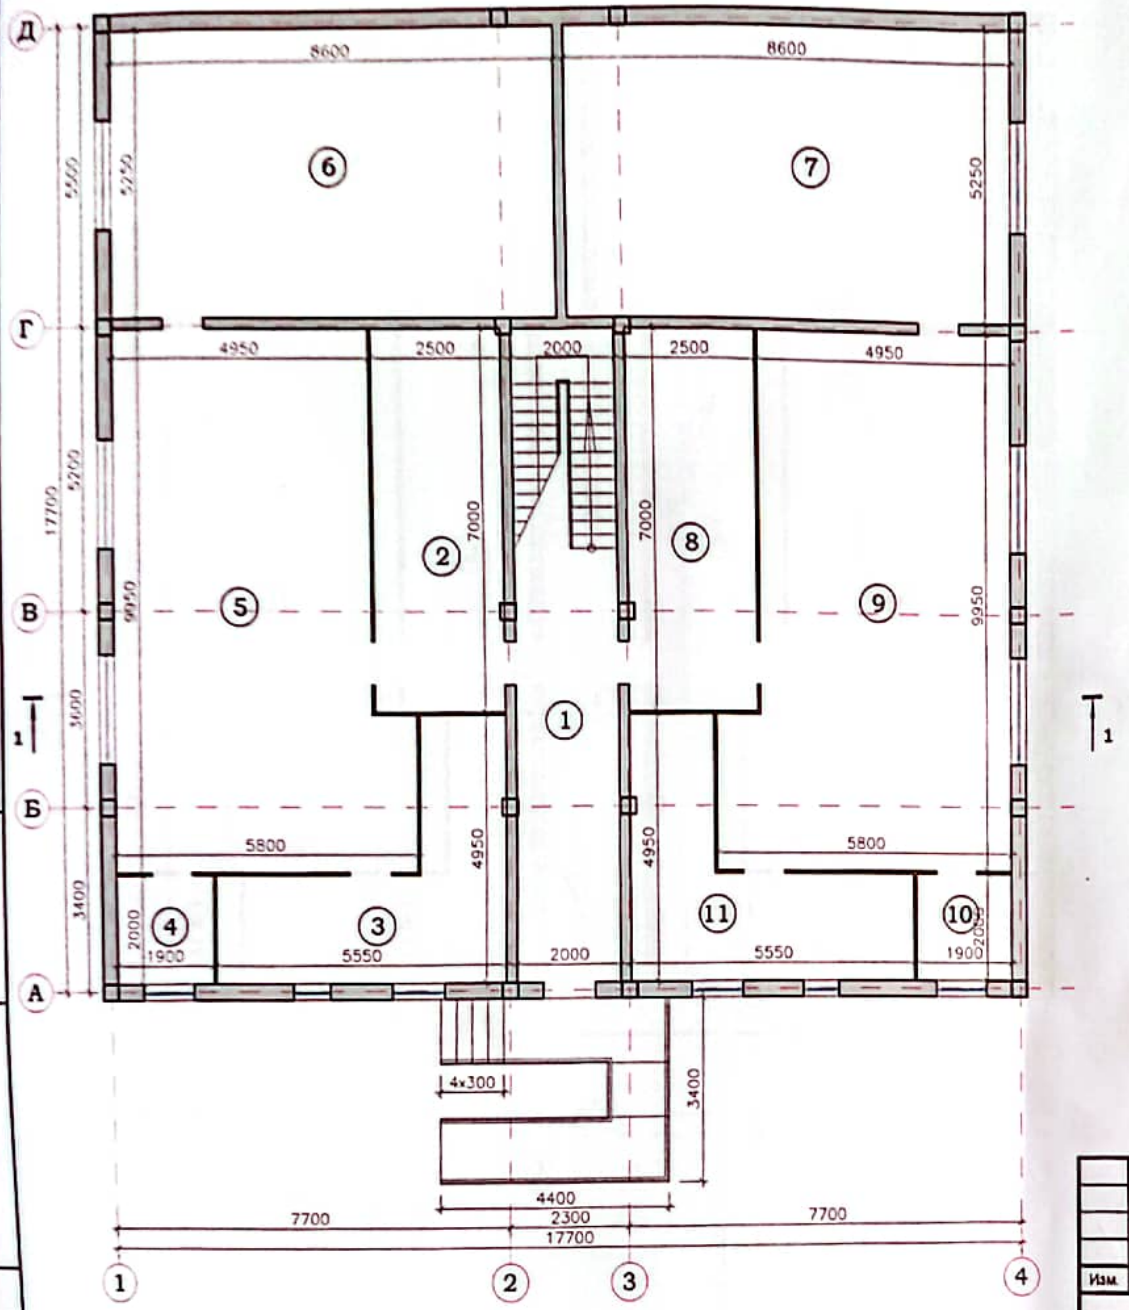

Экспликация помещений

НОМЕР ПОМЕ-ЩЕНИЯ	НАИМЕНОВАНИЕ	ПЛОЩАДЬ М2
1	Коридор	22,0
2	Раздевалка	17,5
3	Сан.узел	16,0
4	Буфетная	3,8
5	Игровая	51,7
6	Спальная	45,1
7	Спальная	45,1
8	Раздевалка	17,5
9	Игровая	51,7
10	Буфетная	3,8
11	Сан.узел	16,0
	Общая площадь:	290,2

Изм.	Кол.уч.	Лист	Nдок.	Подп.	Дата	06-2024-ЭП		
						Алматинская обл. Енбекшиказахский р-н. Каракемерский с/о., с.Талдыбулак, ул.Жамангараев, №77А		
Разработал		Калибеков Б.				Заказчик: Толендиева М.Б.	Стадия	Лист	Листов
							ЭП	2	11
						План на отм. 0.000 М 1:1000	ТОО "ADAL Stroy Limited" Гос.Лиц МКЛ №22002089		

Сканировано с CamScanner

План на отм. 3.000
М 1:1000

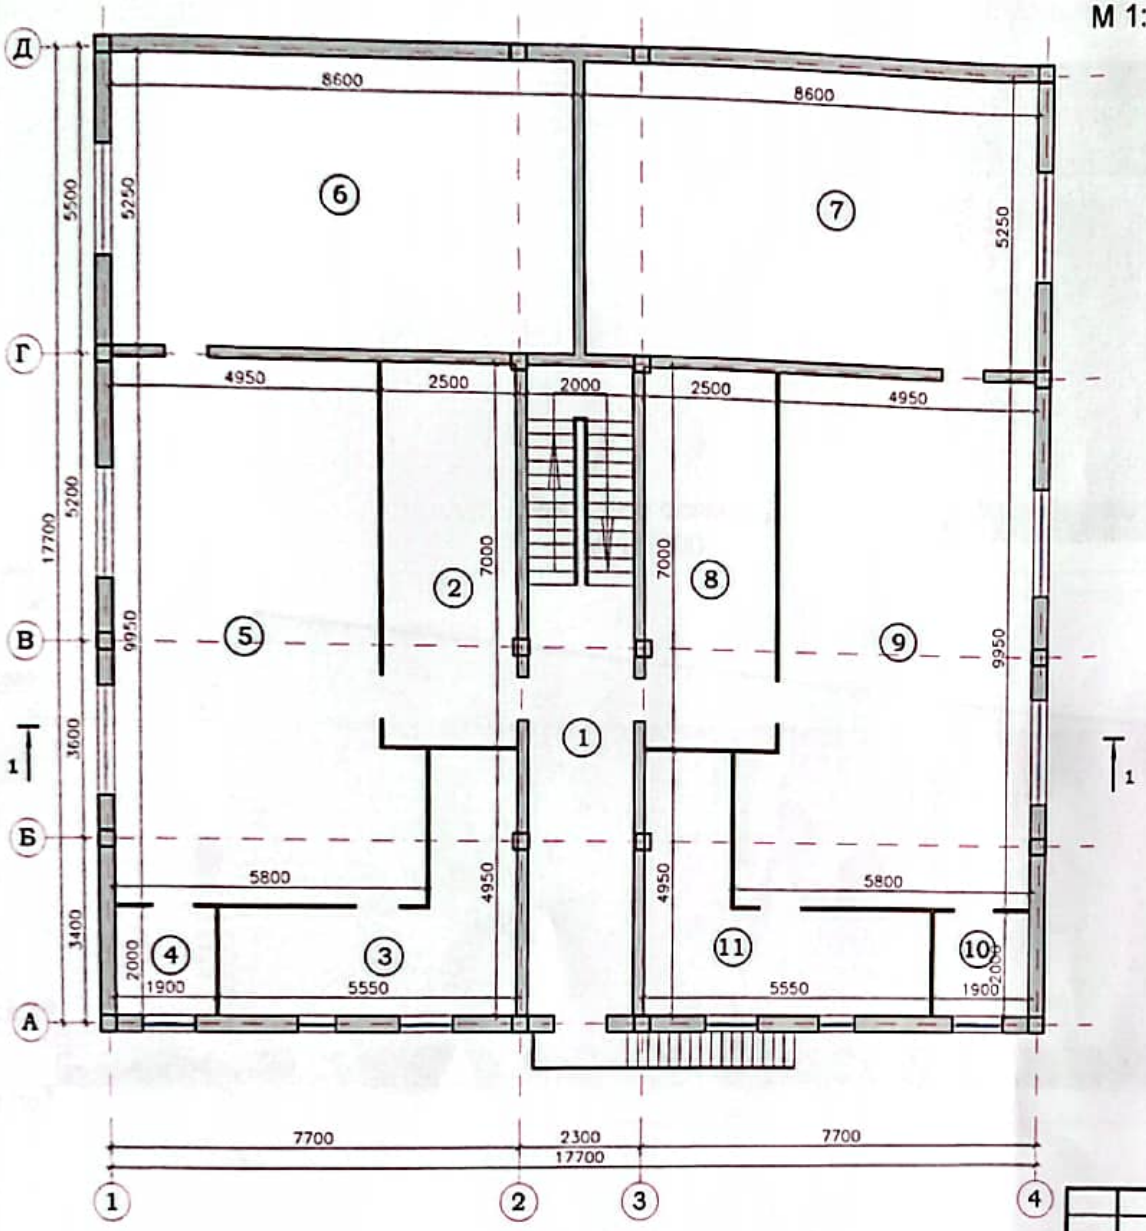

Экспликация помещений

НОМЕР ПОМЕ-ЩЕНИЯ	НАИМЕНОВАНИЕ	ПЛОЩАДЬ М2
1	Коридор	23,6
2	Раздевалка	17,5
3	Сан.узел	16,0
4	Буфетная	3,8
5	Игровая	51,7
6	Спальная	45,1
7	Спальная	45,1
8	Раздевалка	17,5
9	Игровая	51,7
10	Буфетная	3,8
11	Сан.узел	16,0
	Общая площадь:	291,8

Изм.	Кол.уч.	Лист	№док.	Подп.	Дата
Разработал	Калибеков Б.				

06-2024-ЭП

Алматинская обл. Енбекшиказахский р-н.
Каракенерский с/о., с.Талдыбулак, ул.Жамангараев, №77А

Заказчик: Толендиева М.Б.

Стадия	Лист	Листов
ЭП	3	11

План на отм. 3.000
М 1:1000

ТОО "ADAL Stroy Limited"
Гос.Лиц МКЛ №22002089

Сканировано с CamScanner

Фасад по осям 1-4
М 1:1000

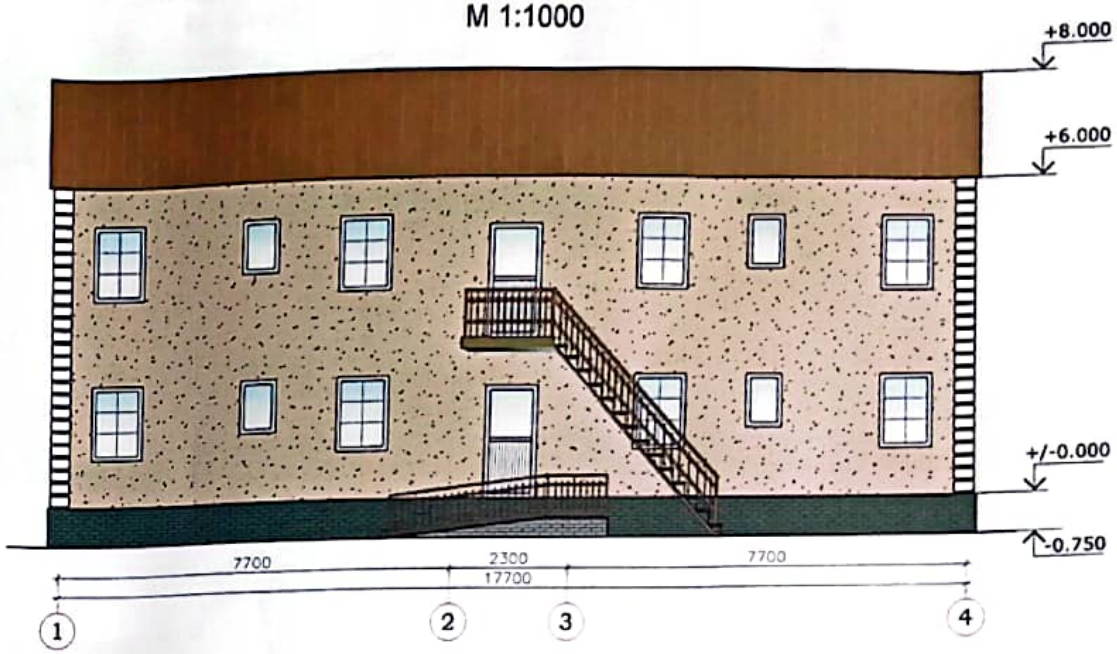

Фасад по осям А-Д
М 1:1000

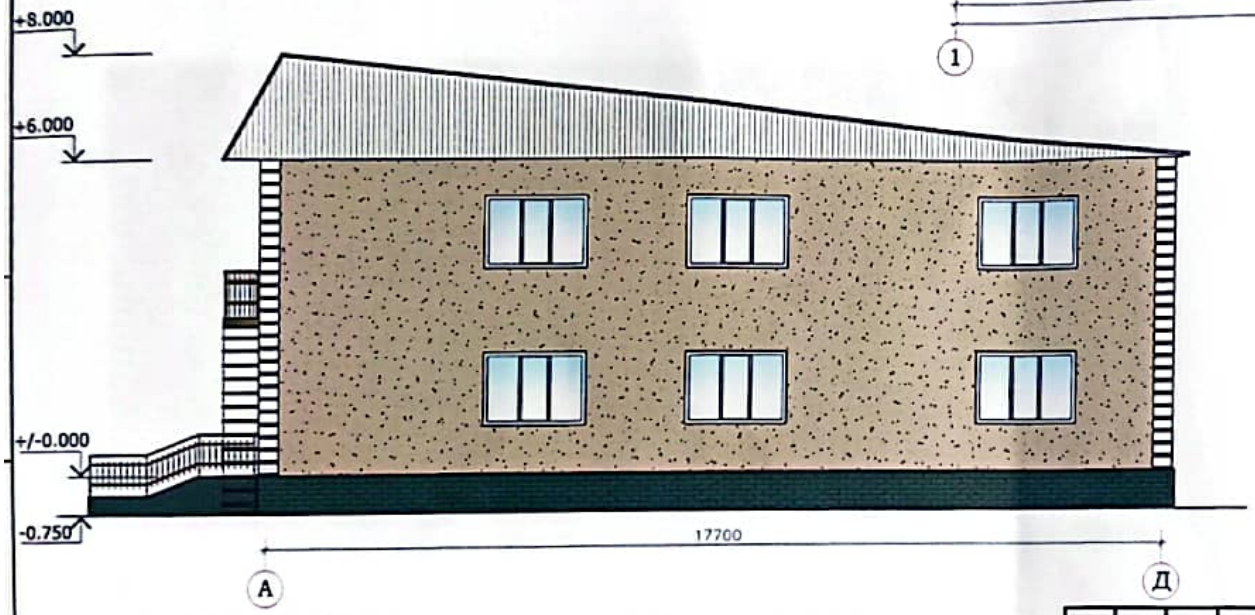

Изм.	Кол.уч	Лист	Nдок.	Подп.	Дата	06-2024-ЭП		
						Алматинская обл. Енбекшиказахский р-н. Каракемерский с/о., с.Талдыбулак, ул.Жамангараев, №77А		
Разработал		Калибеков Б.				Заказчик: Толендиева М.Б.	Стадия	Лист	Листов
							ЭП	4	11
						Фасады М 1:1000	ТОО "ADAL Stroy Limited" Гос.Лиц МКЛ №22002089		

Сканировано с CamScanner

Фасад по осям Д-А
М 1:1000

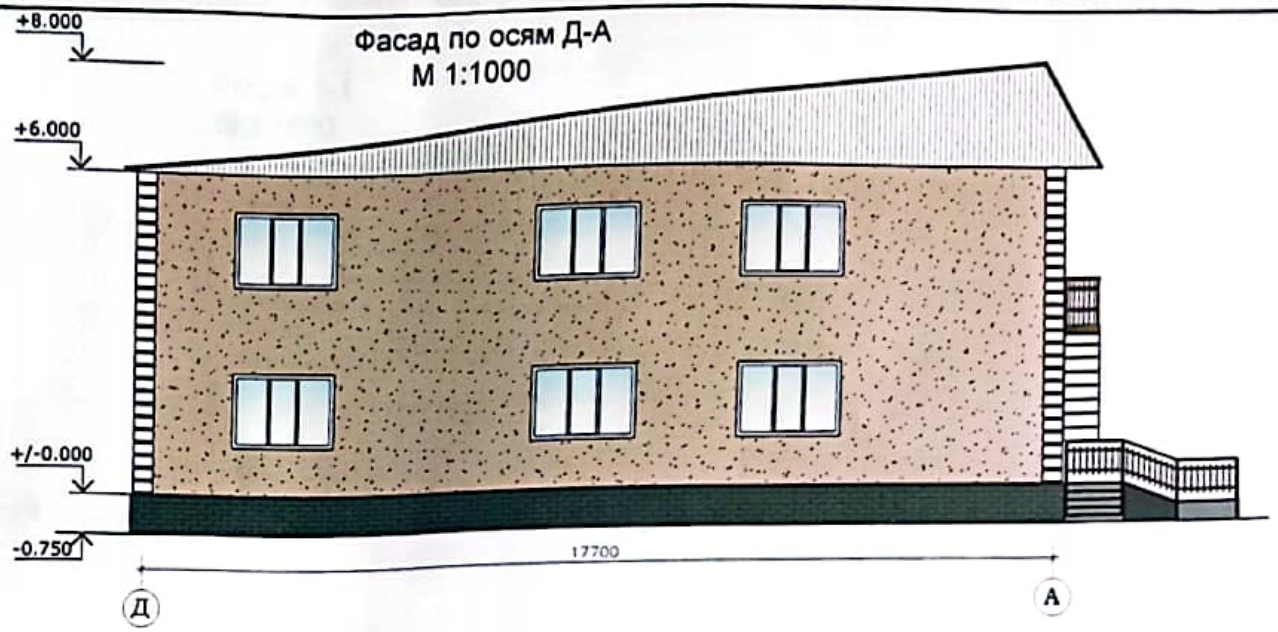

Фасад по осям 4-1
М 1:1000

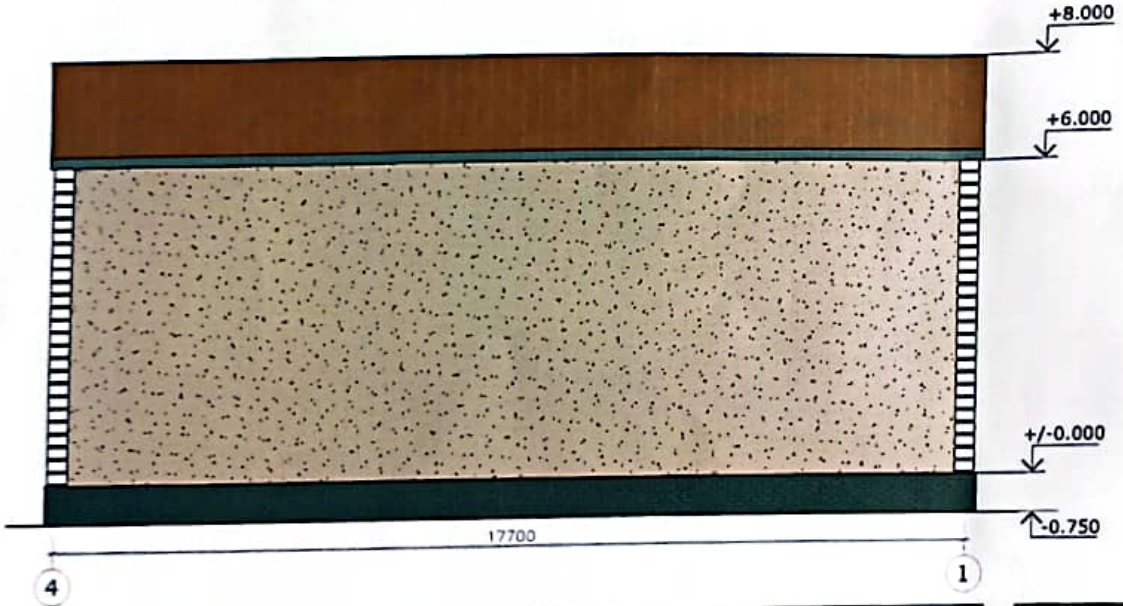

Марка отделки	Элемент фасада	Наименование отделки	Цвет	Площ. м2
1	Цокольная часть здания	декоративный облицовочный кирпич.	Серый	25,2
2	Оконные и дверные откосы	Штукатурка ЦРП "гладкая"	Бежевый	6,3
3	Основные плоскости стен	штукатурка "Мюнхенка"	Бежевый	155,0
4	Металлические элементы (стойки)	Окраска масляной краской по обезжиренной поверхности.	Коричневый	3,3

Изм.	Кол.уч	Лист	№док.	Подп.	Дата
Разработал	Калибеков Б.				

06-2024-ЭП

Алматинская обл. Енбекшиказахский р-н.
Каракемерский с/о., с.Талдыбулак, ул.Жамангараев, №77А

Заказчик: Толендиева М.Б.

Стадия	Лист	Листов
ЭП	5	11

Фасады
М 1:1000

ТОО "ADAL Stroy Limited"
Гос.Лиц МКЛ №22002089

Сканировано с CamScanner

Разрез 1-1
М 1:1000

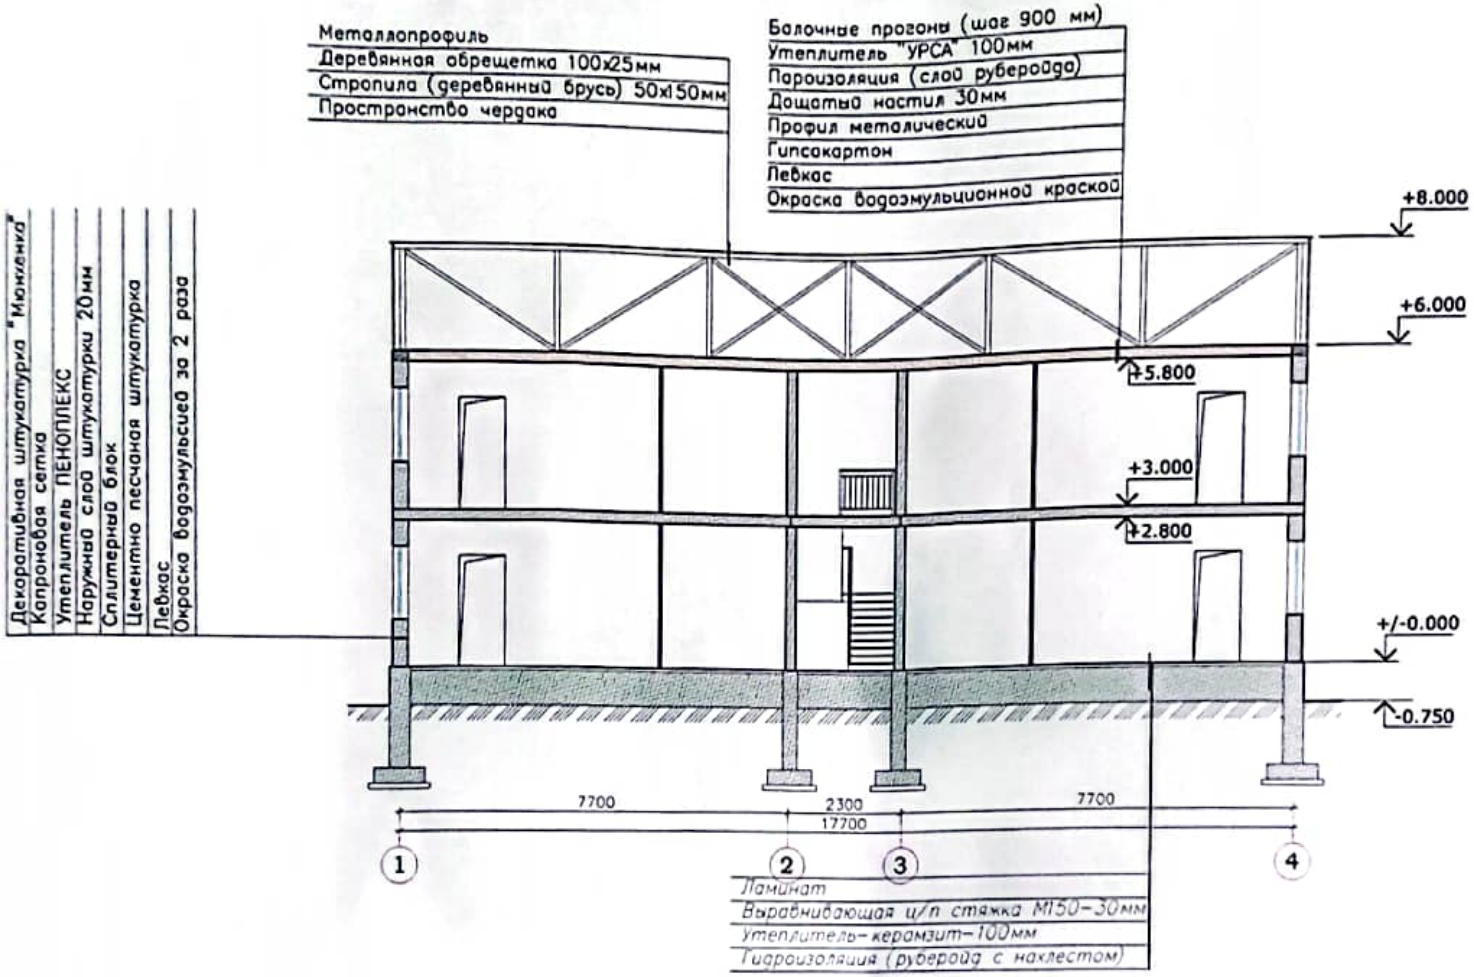

Изм.	Кол.уч.	Лист	Nдок.	Подп.	Дата	06-2024-ЭП
						Алматинская обл. Енбекшиказахский р-н. Каракемерский с/о., с.Талдыбулак, ул.Жамангараев, №77А
Разработал		Калибеков Б.				Заказчик: Толендиева М.Б.
						Стадия: ЭП; Лист: 6; Листов: 11
						Разрез 1-1 М 1:1000
						ТОО "ADAL Stroy Limited" Гос.Лиц МКЛ №22002089

Сканировано с CamScanner

План кровли
М 1:1000

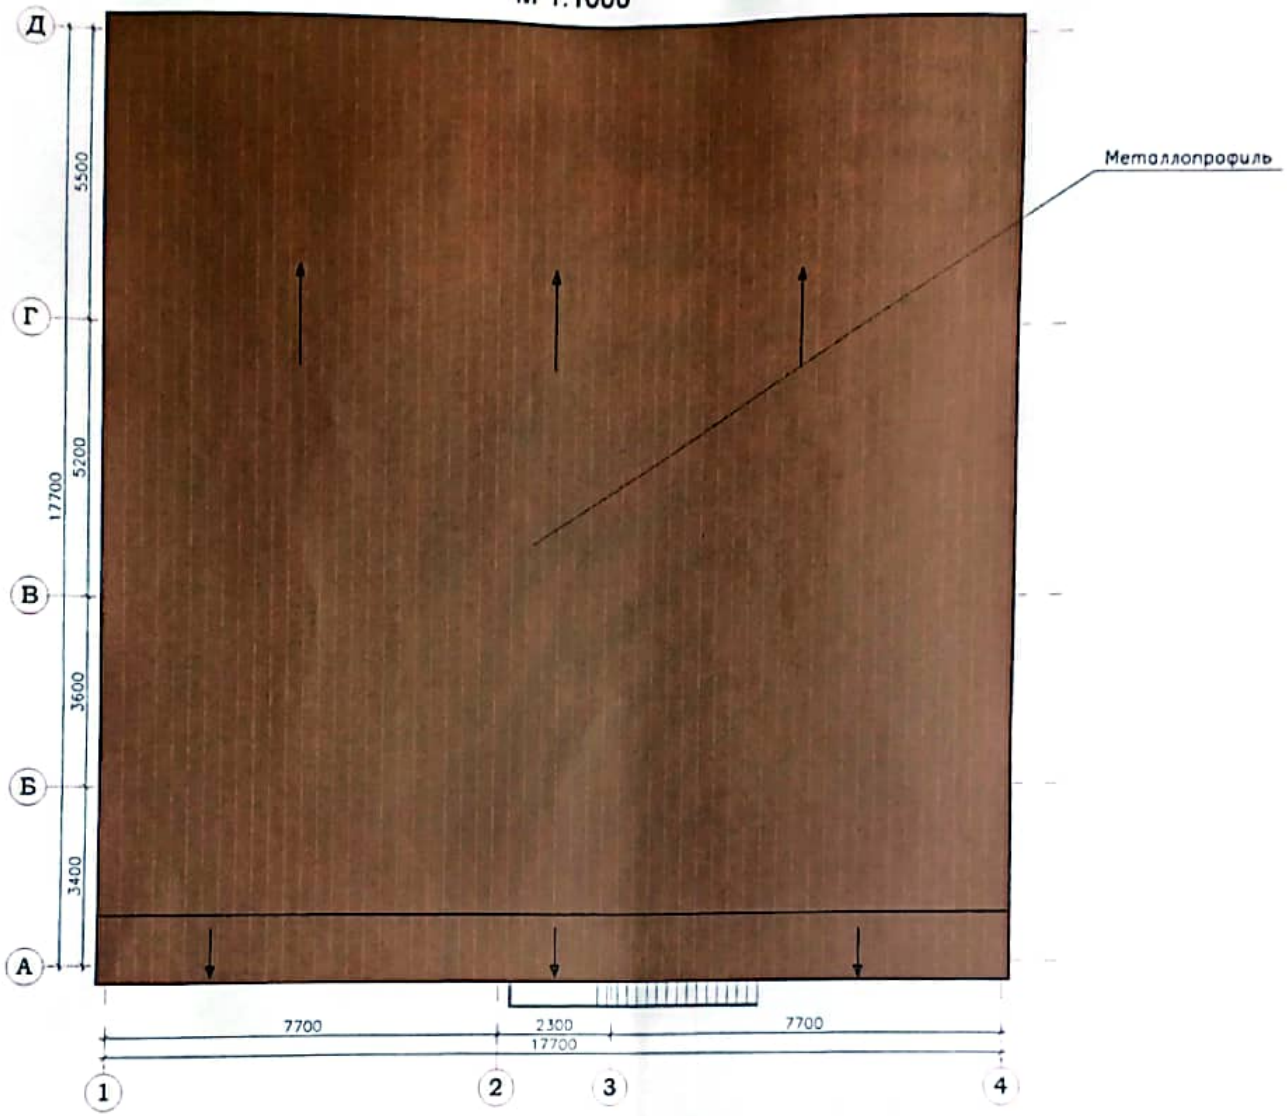

Изм.	Кол.уч.	Лист	№док.	Подп.	Дата	06-2024-ЭП
						Алматинская обл. Енбекшиказахский р-н. Каракемерский с/о., с.Талдыбулак, ул.Жамангараев, №77А
Разработал		Калибеков Б.				Заказчик: Толендиева М.Б.
						План кровли М 1:1000

Стадия	Лист	Листов
ЭП	7	11

ТОО "ADAL Stroy Limited"
Гос.Лиц МКЛ №22002089

Сканировано с CamScanner

План на отм. 0.000
М 1:1000

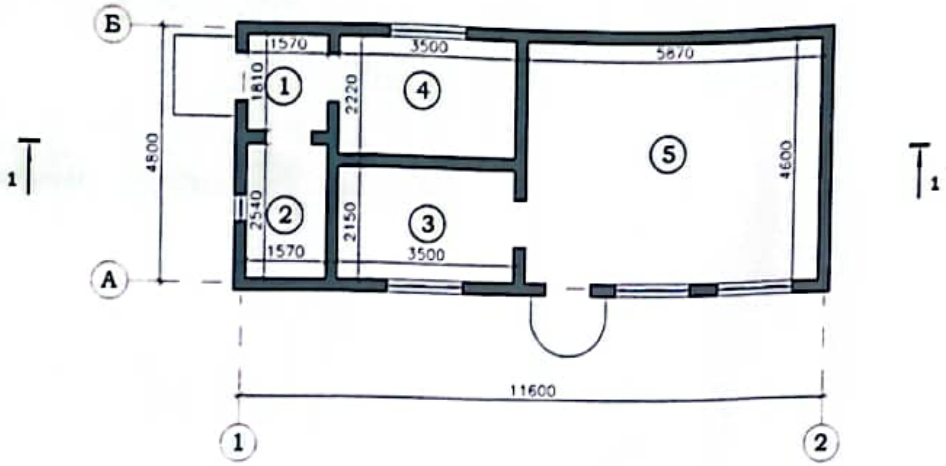

Экспликация помещений

НОМЕР ПОМЕ-ЩЕНИЯ	НАИМЕНОВАНИЕ	ПЛОЩАДЬ М2
1	Прихожая	2,8
2	Склад	3,9
3	Склад для хранения сухой продукции	7,5
4	Склад для хранения овощи	7,7
5	Кухня	27,0
	Общая площадь:	48,9

Изм	Кол.уч	Лист	№док.	Подп.	Дата	06-2024-ЭП		
						Алматинская обл. Енбекшиказахский р-н. Каракемерский с/о., с.Талдыбулак, ул.Жамангараев, №77А		
Разработал		Калибеков Б.				Заказчик: Толендиева М.Б.	Стадия: ЭП	Лист: 8 / Листов: 11
						План на отм. 0.000 М 1:1000	ТОО "ADAL Stroy Limited" Гос.Лиц МКЛ №22002089	

Сканировано с CamScanner

Фасад по осям 1-2
М 1:1000

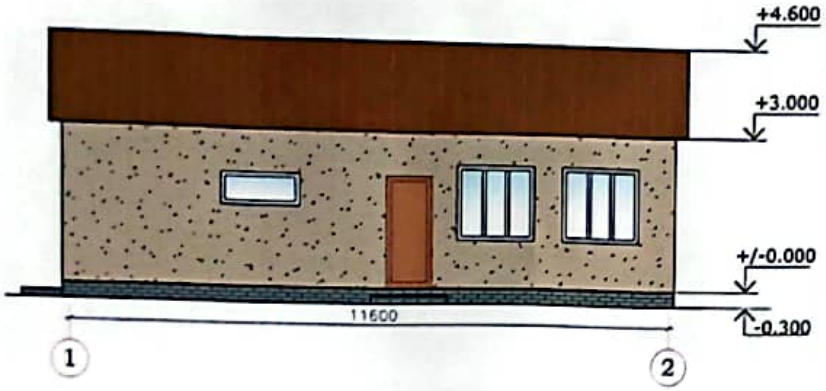

Фасад по осям А-Б
М 1:1000

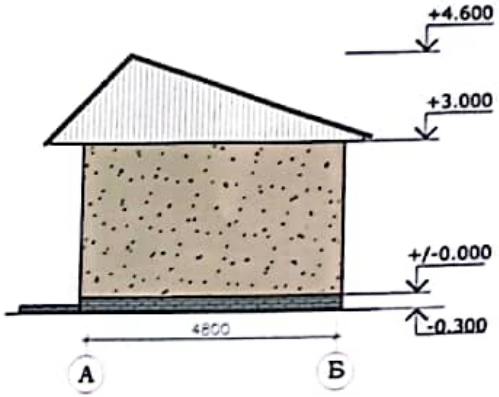

Фасад по осям 2-1
М 1:1000

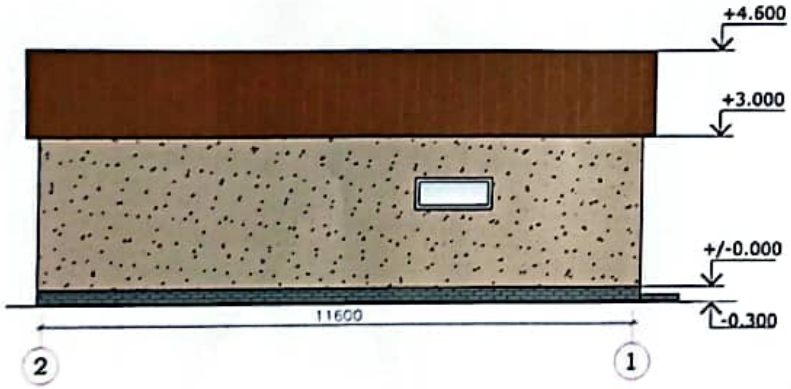

Фасад по осям Б-А
М 1:1000

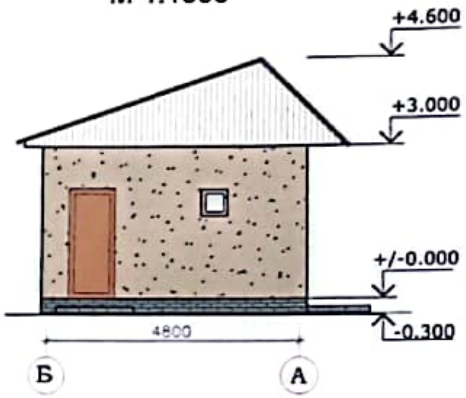

Изм.	Кол уч	Лист	Nдок.	Подп.	Дата	06-2024-ЭП		
						Алматинская обл. Енбекшиказахский р-н. Каракемерский с/о., с.Талдыбулак, ул.Жамангараев, №77А		
Разработал	Калибеков Б.					Заказчик Толендиева М.Б.	Стадия	Лист	Листов
							ЭП	9	11
						Фасады М 1:1000	ТОО "ADAL Stroy Limited" Гос.Лиц МКЛ №22002089		

Сканировано с CamScanner

Разрез 1-1
М 1:1000

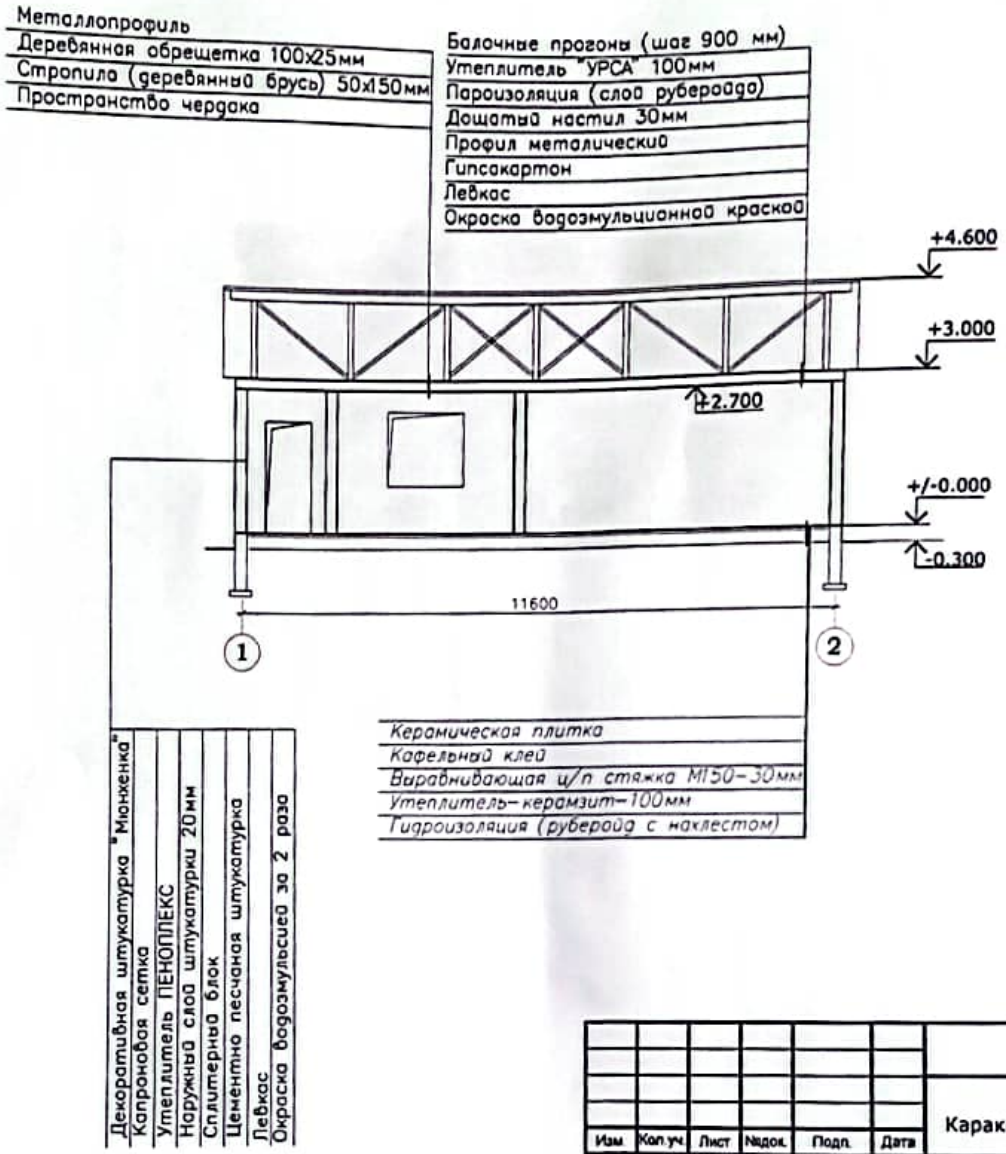

Изм.	Кол.уч.	Лист	№док.	Подп.	Дата
Разработал		Калибеков Б.			

06-2024-ЭП

Алматинская обл. Енбекшиказахский р-н.
Каракемерский с/о., с.Талдыбулак, ул.Жамангараев, №77А

Заказчик: Топендиева М.Б.

Стадия	Лист	Листов
ЭП	10	11

Разрез 1-1
М 1:1000

ТОО "ADAL Stroy Limited"
Гос.Лиц МКЛ №22002089

Сканировано с CamScanner

План кровли
М 1:1000

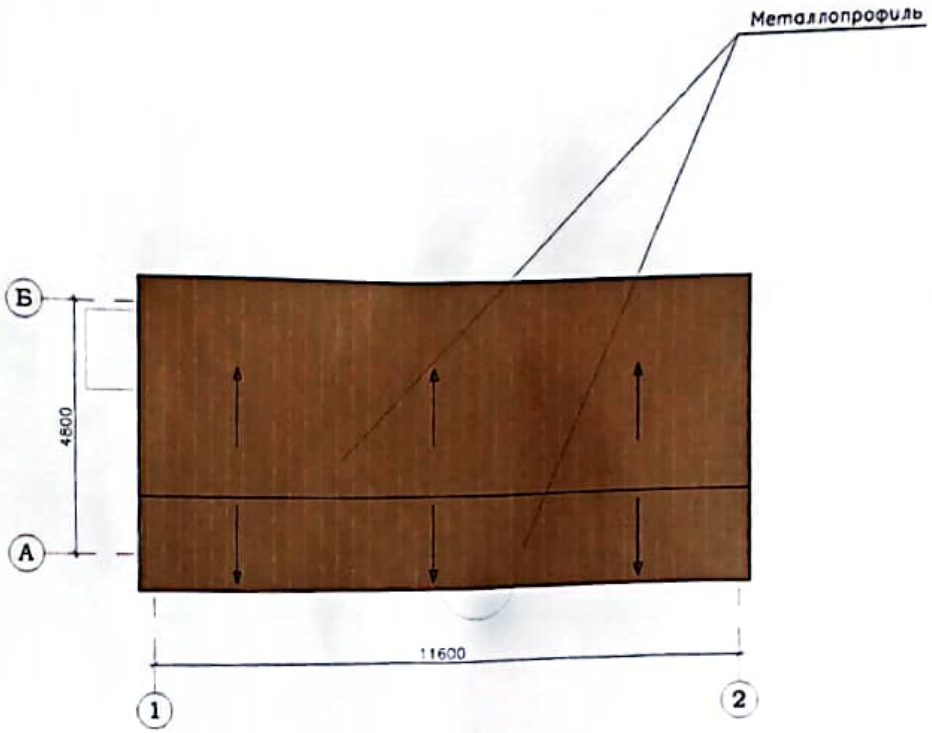

Изм.	Кол уч	Лист	№док.	Подп.	Дата	06-2024-ЭП
						Алматинская обл. Енбекшиказахский р-н. Каракемерский с/о., с.Талдыбулак, ул.Жамангараев, №77А
Разработал		Калибеков Б.				Заказчик: Толендиева М.Б.
						План кровли М 1:1000

Стадия	Лист	Листов
ЭП	11	11

ТОО "ADAL Stroy Limited"
Гос.Лиц МКЛ №22002089

Сканировано с CamScanner